



CERTIFICATIE VAN

GIETIJZEREN WEGENISPRODUCTEN

BENOR

Deze technische fiche werd afgedrukt op 2/03/2026.
De geldigheid van deze fiche kan nagekeken worden op
<http://extranet.copro.eu/>



TECHNISCHE FICHE

SNELCODE	VERSIE	GELDIGHEID
0453/0025	3.0 - 27/02/2026	GECERTIFICEERD
CERTIFICAATHOUDER	PRODUCTIEEENHEID	CERTIFICAATNUMMER
VYANZO Botermelkbaan 51 BE-2900 Schoten steve@vyanzo.be	RBA Ferro Industries Private Limited 2/6 Sarat Bose Road, Central Plaza IN-700020 Kolkata, West Bengal +91 33 24 85 87 55 harsh@rbaferro.com	BENOR 0453/80B Gietijzeren wegenisproducten

PRODUCT

OFFICIËLE BENAMING	COMMERCIEËLE BENAMING
STRAATKOLK PLAT D4DQ	V30/60Z

OPSCHRIFT OP HET PRODUCT

- naam en/of logo van de producent : Vyanzo
- EN 124-2, klasse D400
- PTV 802 Q en het BENOR-merk
- identificatienummer van de producent : 453
- datum of lotnummer van de productie
- type gietijzer (GJS)
- productiejaar
- Buitendiameter van de uitgang van de straatkolk: 156mm

TOEPASSING

- | | | |
|--|---|---|
| ☐ CCT/TB 2015 | ☒ PTV 802 (9.0) | ☒ EN 124-2 (2015) |
| ☐ SB 250 - versie 4.1 | | ☒ EN 124-1 (2015) |
| ☐ CCT-Qualiroutes (2021) | | |
| ☒ SB 250 - versie 4.1 + errata | | |

Dit product werd niet nagekeken volgens de doorstreepte referentiedocumenten of voldoet er niet aan.

Gebruik: Groep 3 : Plaatsing in de zone van de straatgreppels langs de voetpaden en die, gmeten vanaf de boordsteen van het voetpad, max tot 0,5 m in de rijweg en tot 0,2 m in het voetpad liggen.

TOELICHTINGEN (DIT VALT NIET ONDER HET EXTERN TOEZICHT IN HET KADER VAN DE BENOR-CERTIFICATIE)

AANDACHTSPUNTEN - NOG TE CONTROLEREN DOOR DE AFNEMER (NIET LIMITATIEF)

De fabrikaten vertonen geen gietfouten en geen breuken of geen braam.
De identificatie is volledig en duidelijk leesbaar.
Straatkolken waarvan de doorstroomcapaciteit is bepaald behoren tot de klasse "Q".
Straatkolken waarvan de doorstroomcapaciteit niet is bepaald behoren tot de klasse "X".

TOELEVERINGSVORM

Rooster(s) en straatkolk worden als geheel geleverd.

EXTRA INFORMATIE

COPRO- en BENOR-materialen mogen onderling niet gemengd worden.
Een elastische oplegging voldoet aan de eisen van PTV 832-5.

Contactpersoon bij


* COPRO:	Kris Vandenneucker	+32 2 468 00 95	kris.vandenneucker@copro.eu
* Certificaathouder:	Steve Vernelen		steve@vyanzo.be

PRODUCTEIGENSCHAPPEN


GIETIJZERKWALITEIT	VOLGENS	EENHEID	WAARDE	MIN	MAX
<i>Treksterkte</i>	EN ISO 6892-1	MPa	-	500	-
<i>Rek bij breuk</i>	EN ISO 6892-1	%	-	7	-
MECHANISCHE EIGENSCHAPPEN	VOLGENS	EENHEID	WAARDE	MIN	MAX
<i>Blijvende doorbuiging</i>	NBN EN 124-1	mm	-	-	1,0
<i>Controlebelasting</i>	NBN EN 124-1	kN	geen breuk	344	-
GEOMETRIE	VOLGENS	EENHEID	WAARDE	MIN	MAX
<i>Breedte</i>		mm	295	-	-
<i>Capaciteit van de straatkolk</i>	PTV 802	l	46	-	-
<i>Hoogte</i>		mm	600	-	-
<i>Openingsmaat</i>	NBN EN 124-1	mm	215	-	-
HYDRAULISCHE EIGENSCHAPPEN	VOLGENS	EENHEID	WAARDE	MIN	MAX
<i>Doorstroomcapaciteit van de straatkolk</i>	PTV 802	l/s	-	-	48
OVERIGE EIGENSCHAPPEN	VOLGENS	EENHEID	WAARDE	MIN	MAX
<i>Gewicht van het rooster - "rond"</i>		kg	-	21	-
<i>Gewicht van het rooster - "recht"</i>		kg	-	26	-
<i>Gewicht van het rooster - "45°"</i>		kg	-	23	-
<i>Gewicht van de kuip</i>		kg	-	104	-

TECHNISCHE TEKENING


3. V30/60Z-OBLIQUE FLAT

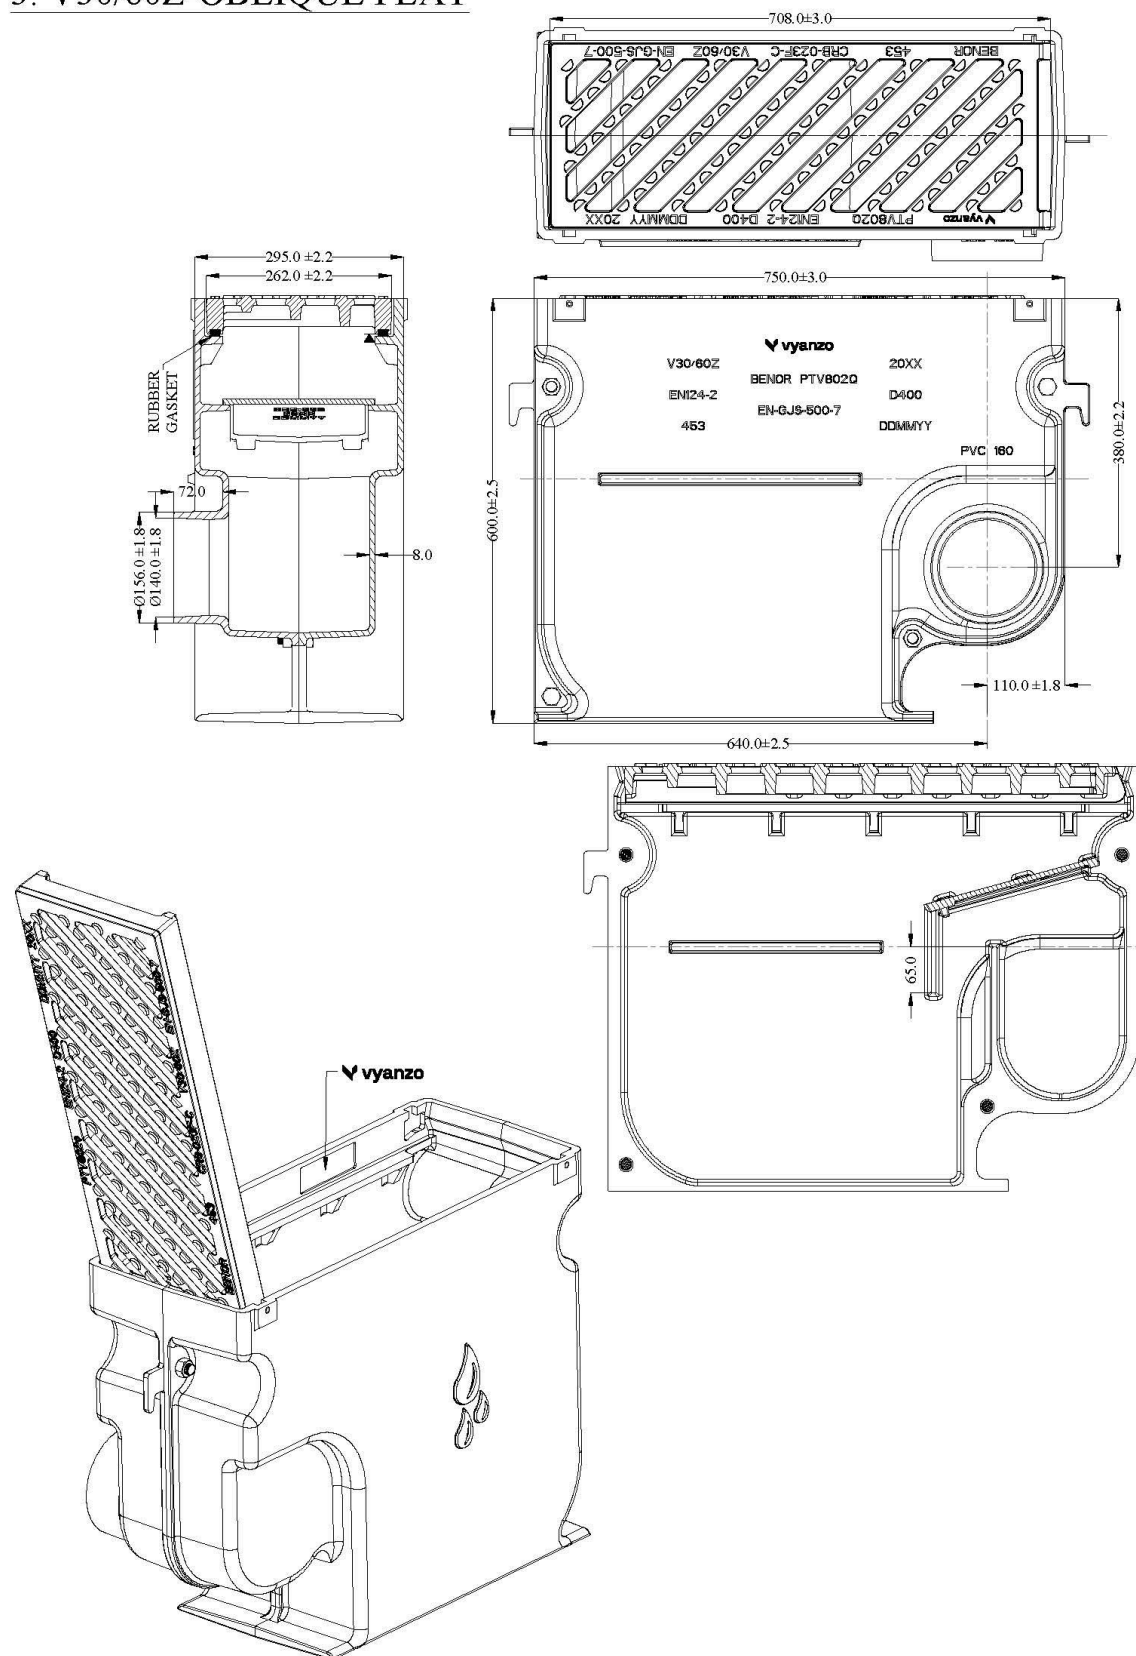

1. V30/60Z-ROUND FLAT

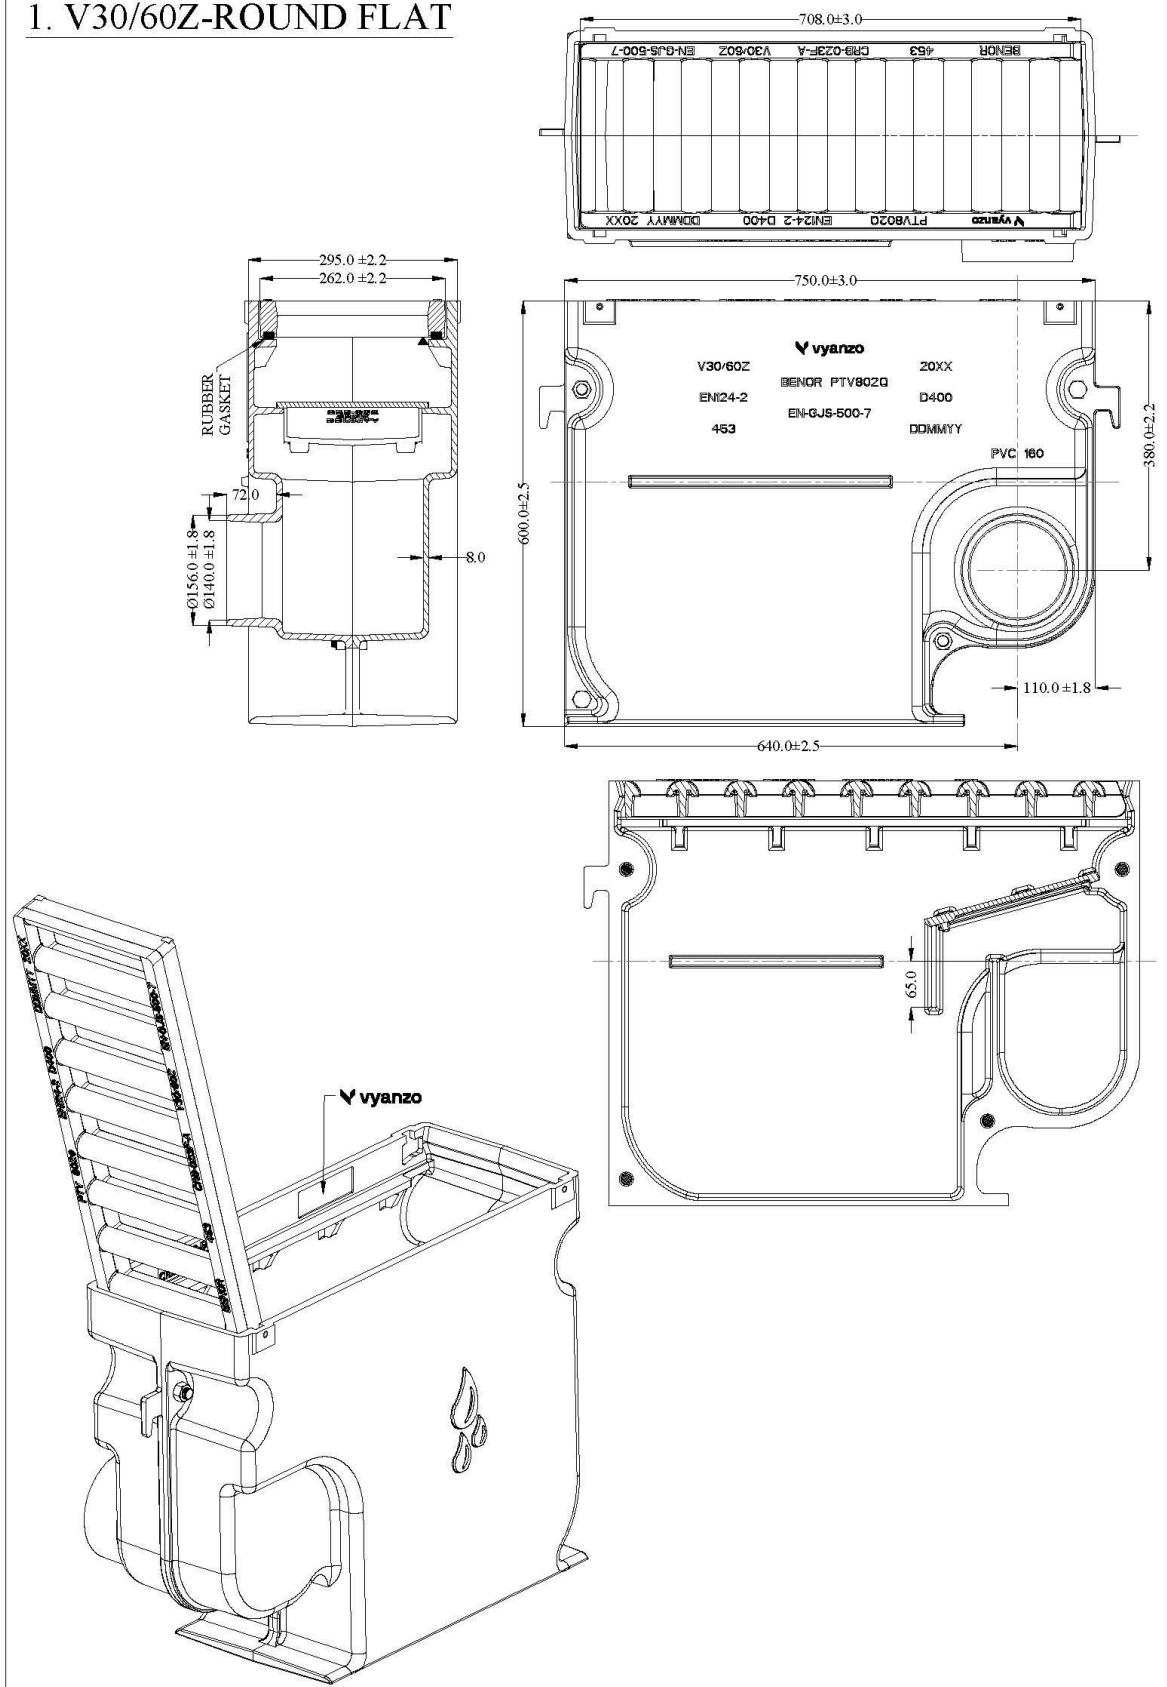

2. V30/60Z-STRAIGHT FLAT

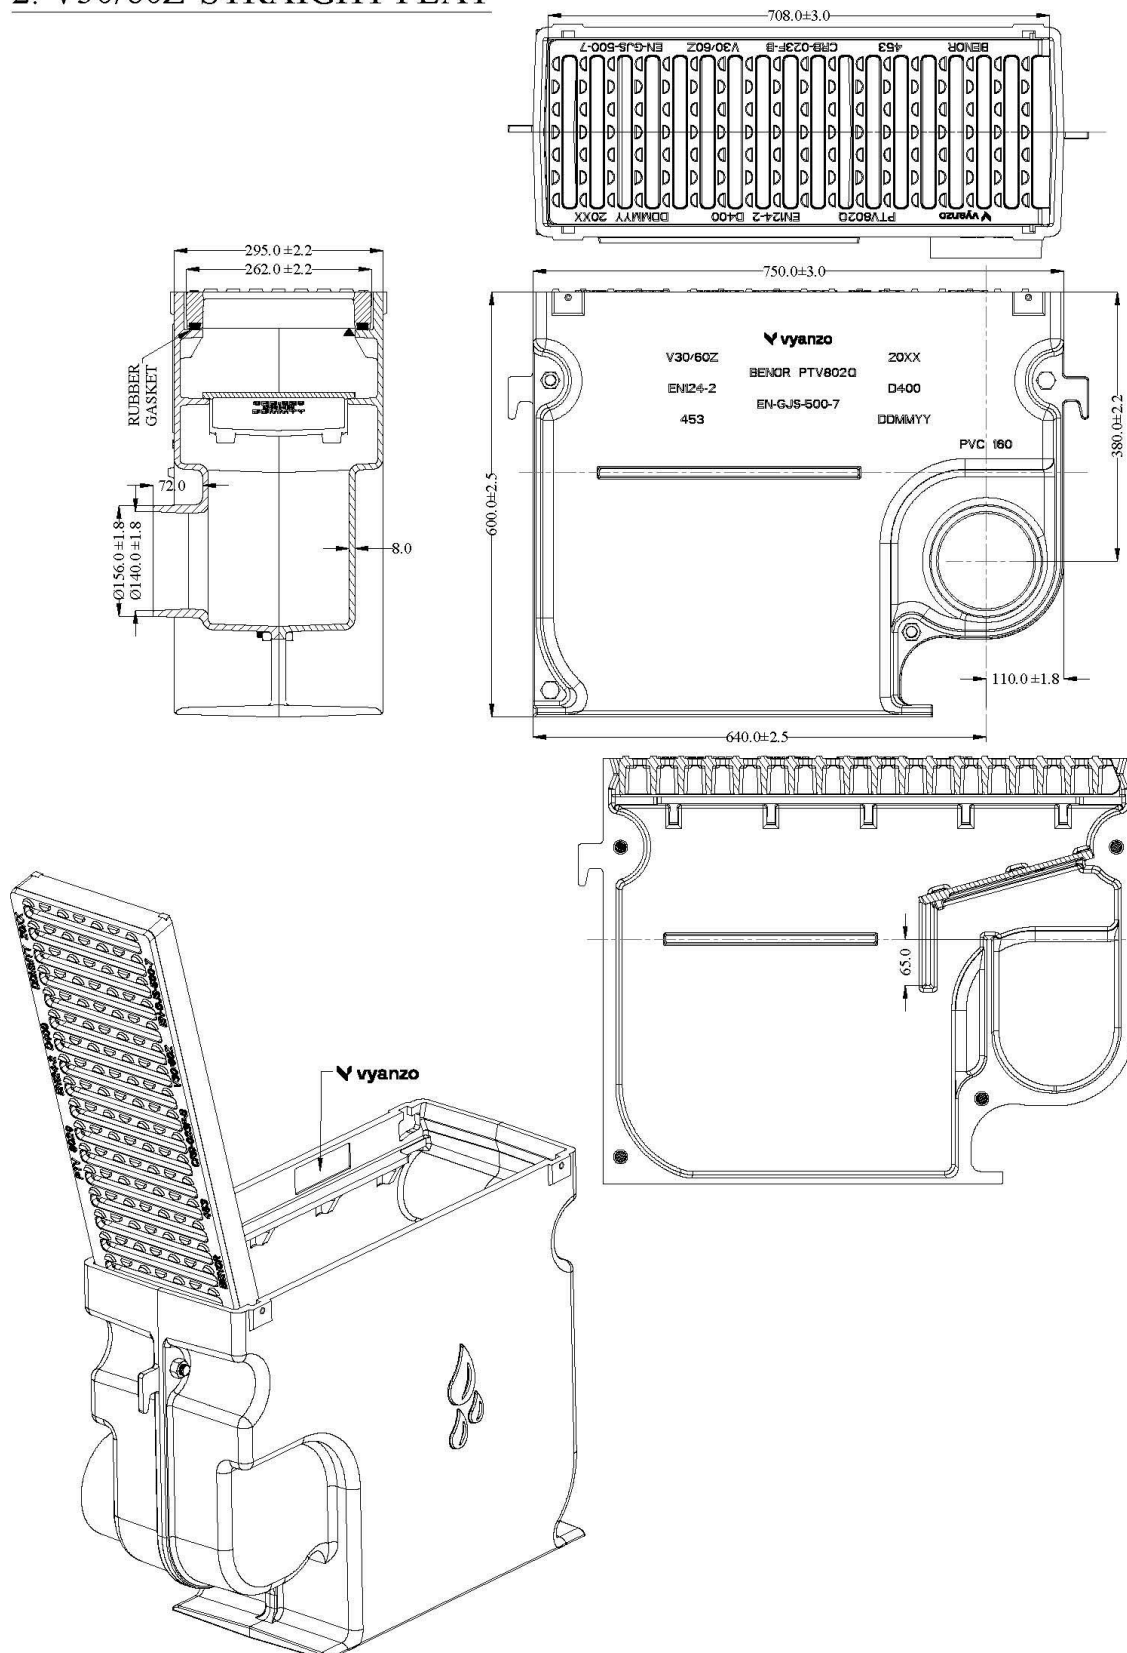

WAARMERKING

De BENOR-certificatie van het product geeft aan dat op basis van een periodiek extern toezicht een voldoende mate van vertrouwen bestaat dat de certificaathouder in staat is om doorlopend de conformiteit van het product, zoals vastgelegd in de referentiedocumenten en in TRA 80 BENOR (8.0) te waarborgen.

Deze technische fiche bevat de prestaties van kenmerken die door de producent verklaard worden. De technische fiche wordt door de certificatie-instelling geverifieerd.

De certificaathouder verklaart een product te leveren dat conform is aan deze technische fiche zoals vermeld op de leveringsbon.

Door het digitaal beschikbaar stellen verklaart de producent zich akkoord met deze fiche

Naam: Steve Vernelen

Datum: 26/02/2026

COPRO

Naam: Kris Vandenneucker

Datum: 27/02/2026

Handtekening:



COPRO vzw - Z.1 Researchpark - Kranenberg 190 - B-1731
Zellik